

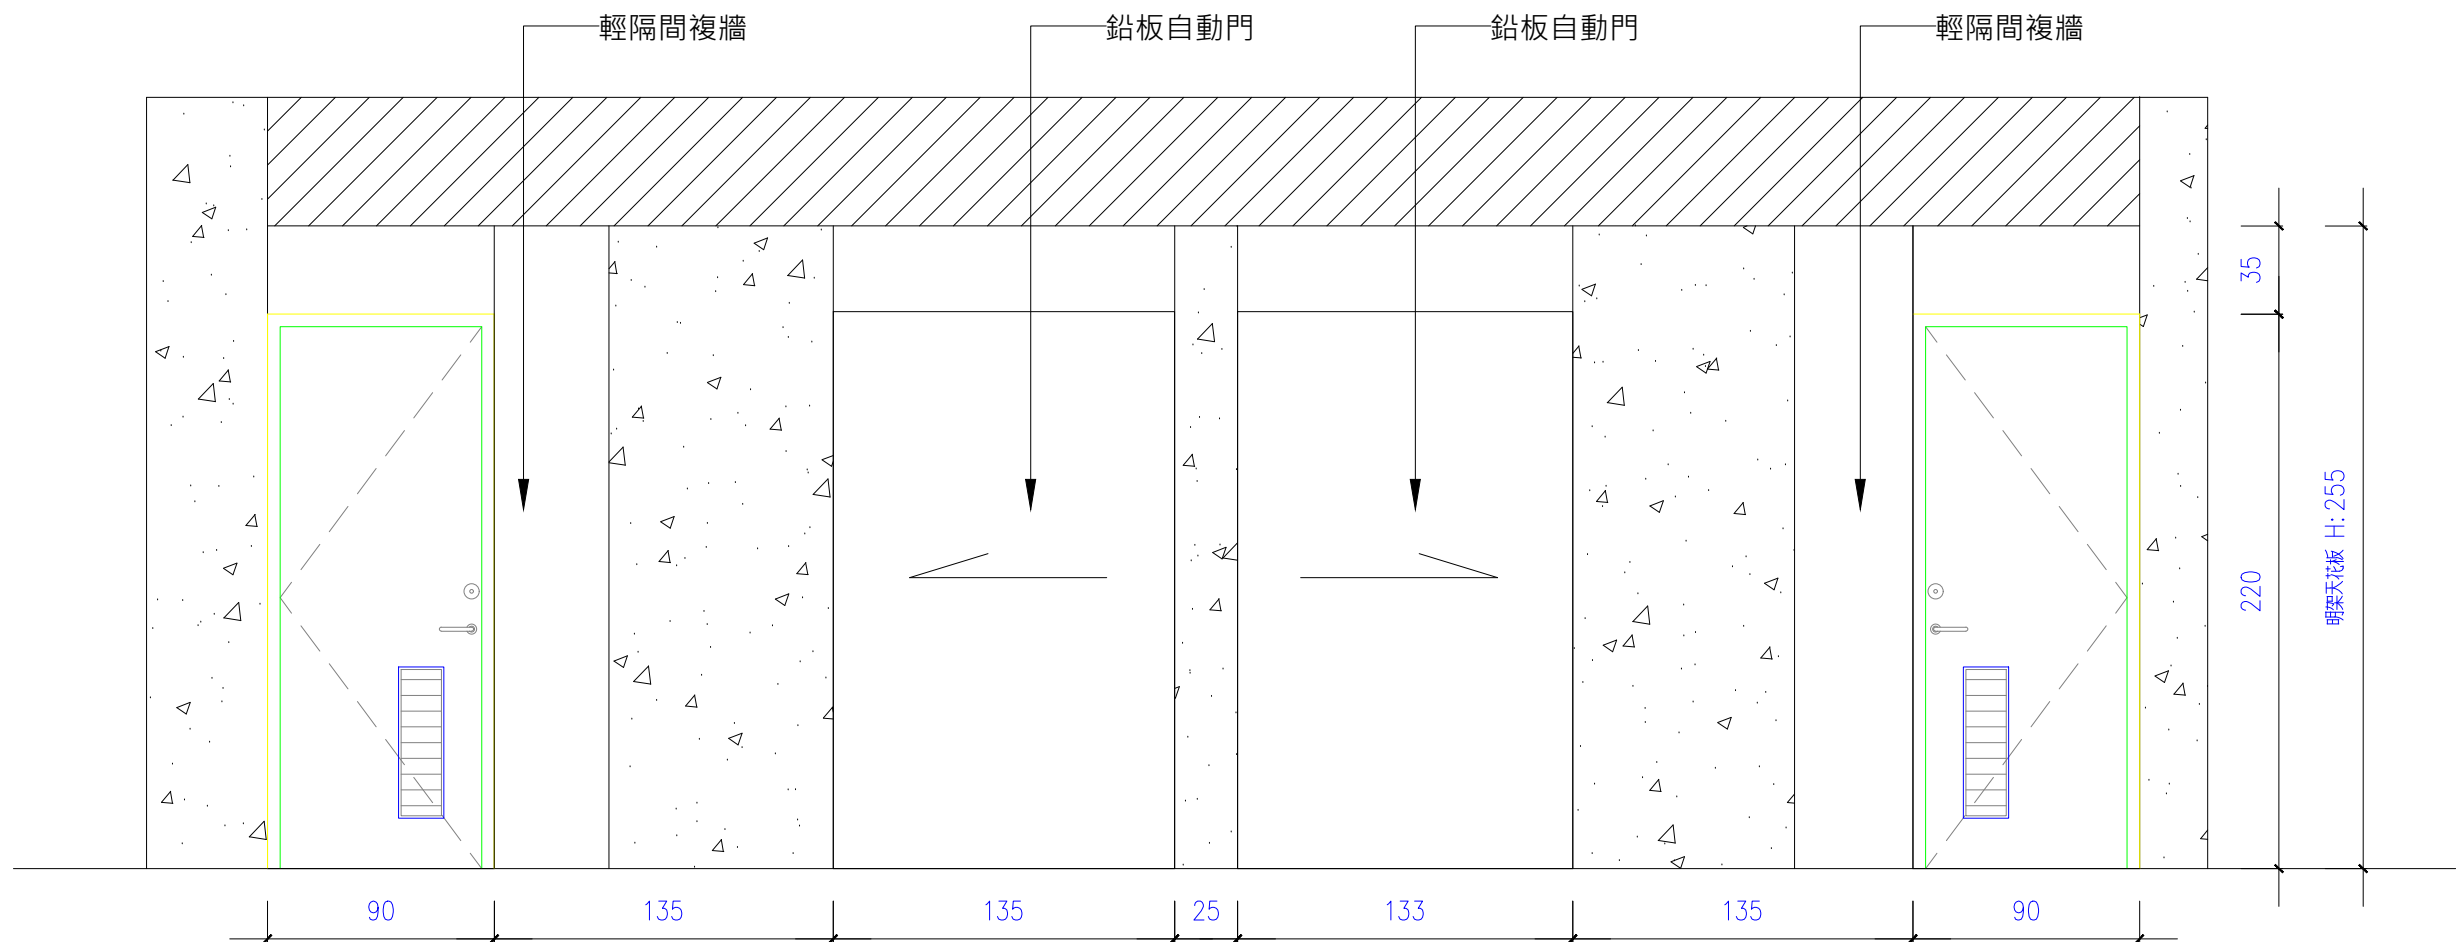


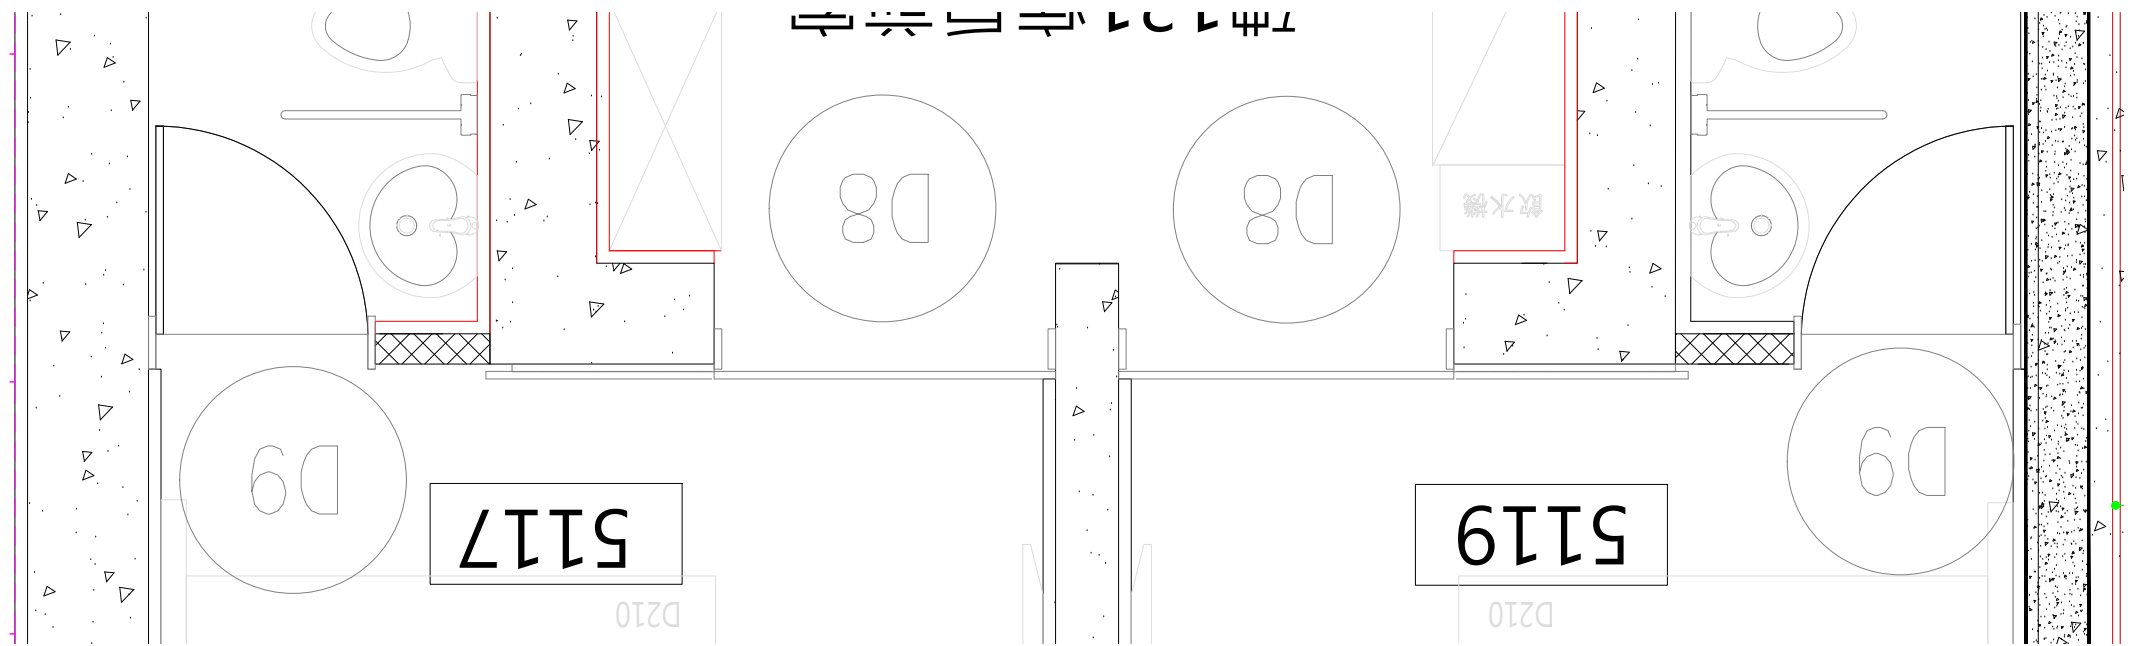


*圖面尺寸為現場尺寸

D8鉛門平面圖(施工詳圖參考1-1)▼

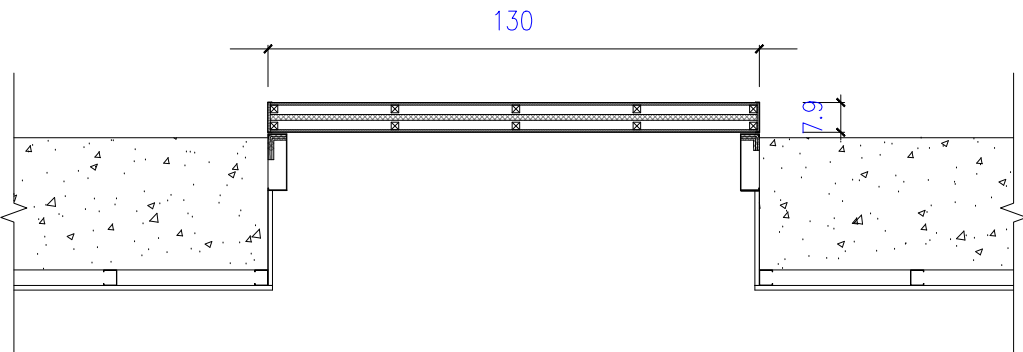


6mm鍍鋅鋼板
2*2cm方管
1.5cm鉛皮

D8鉛門剖面圖▶

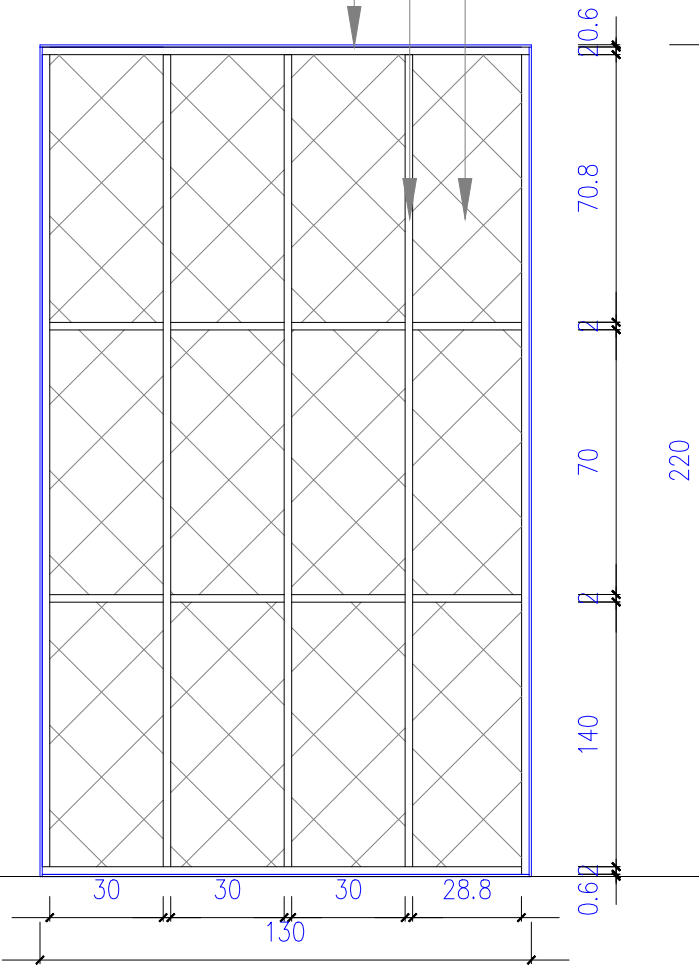

施工詳圖1-1▶

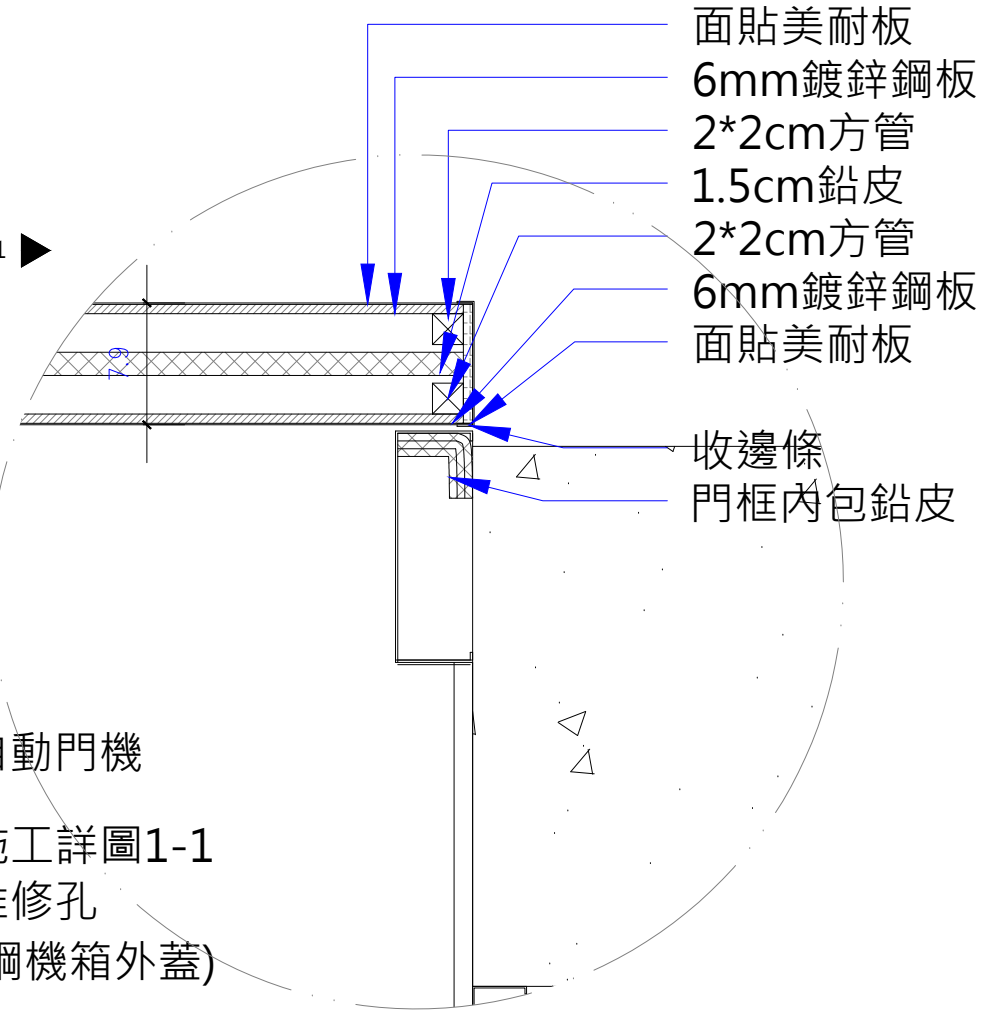

重型自動門機
參考施工詳圖1-1
上掀維修孔
(不鏽鋼機箱外蓋)

面貼美耐板
6mm鍍鋅鋼板
2*2cm方管
1.5cm鉛皮
水泥砂漿嵌縫填塞
2*2cm方管
6mm鍍鋅鋼板
面貼美耐板

D8鉛門側剖面圖▶

